
TIPO DE SUMINISTRO: Cambio tensión
DIRECCIÓN: Calle SAN MATEO, 17, Bajo ASCN
T.M: MADRID
MUNICIPIO: MADRID
POTENCIA: 73,5 Kw
Nº EXP: 9045838454

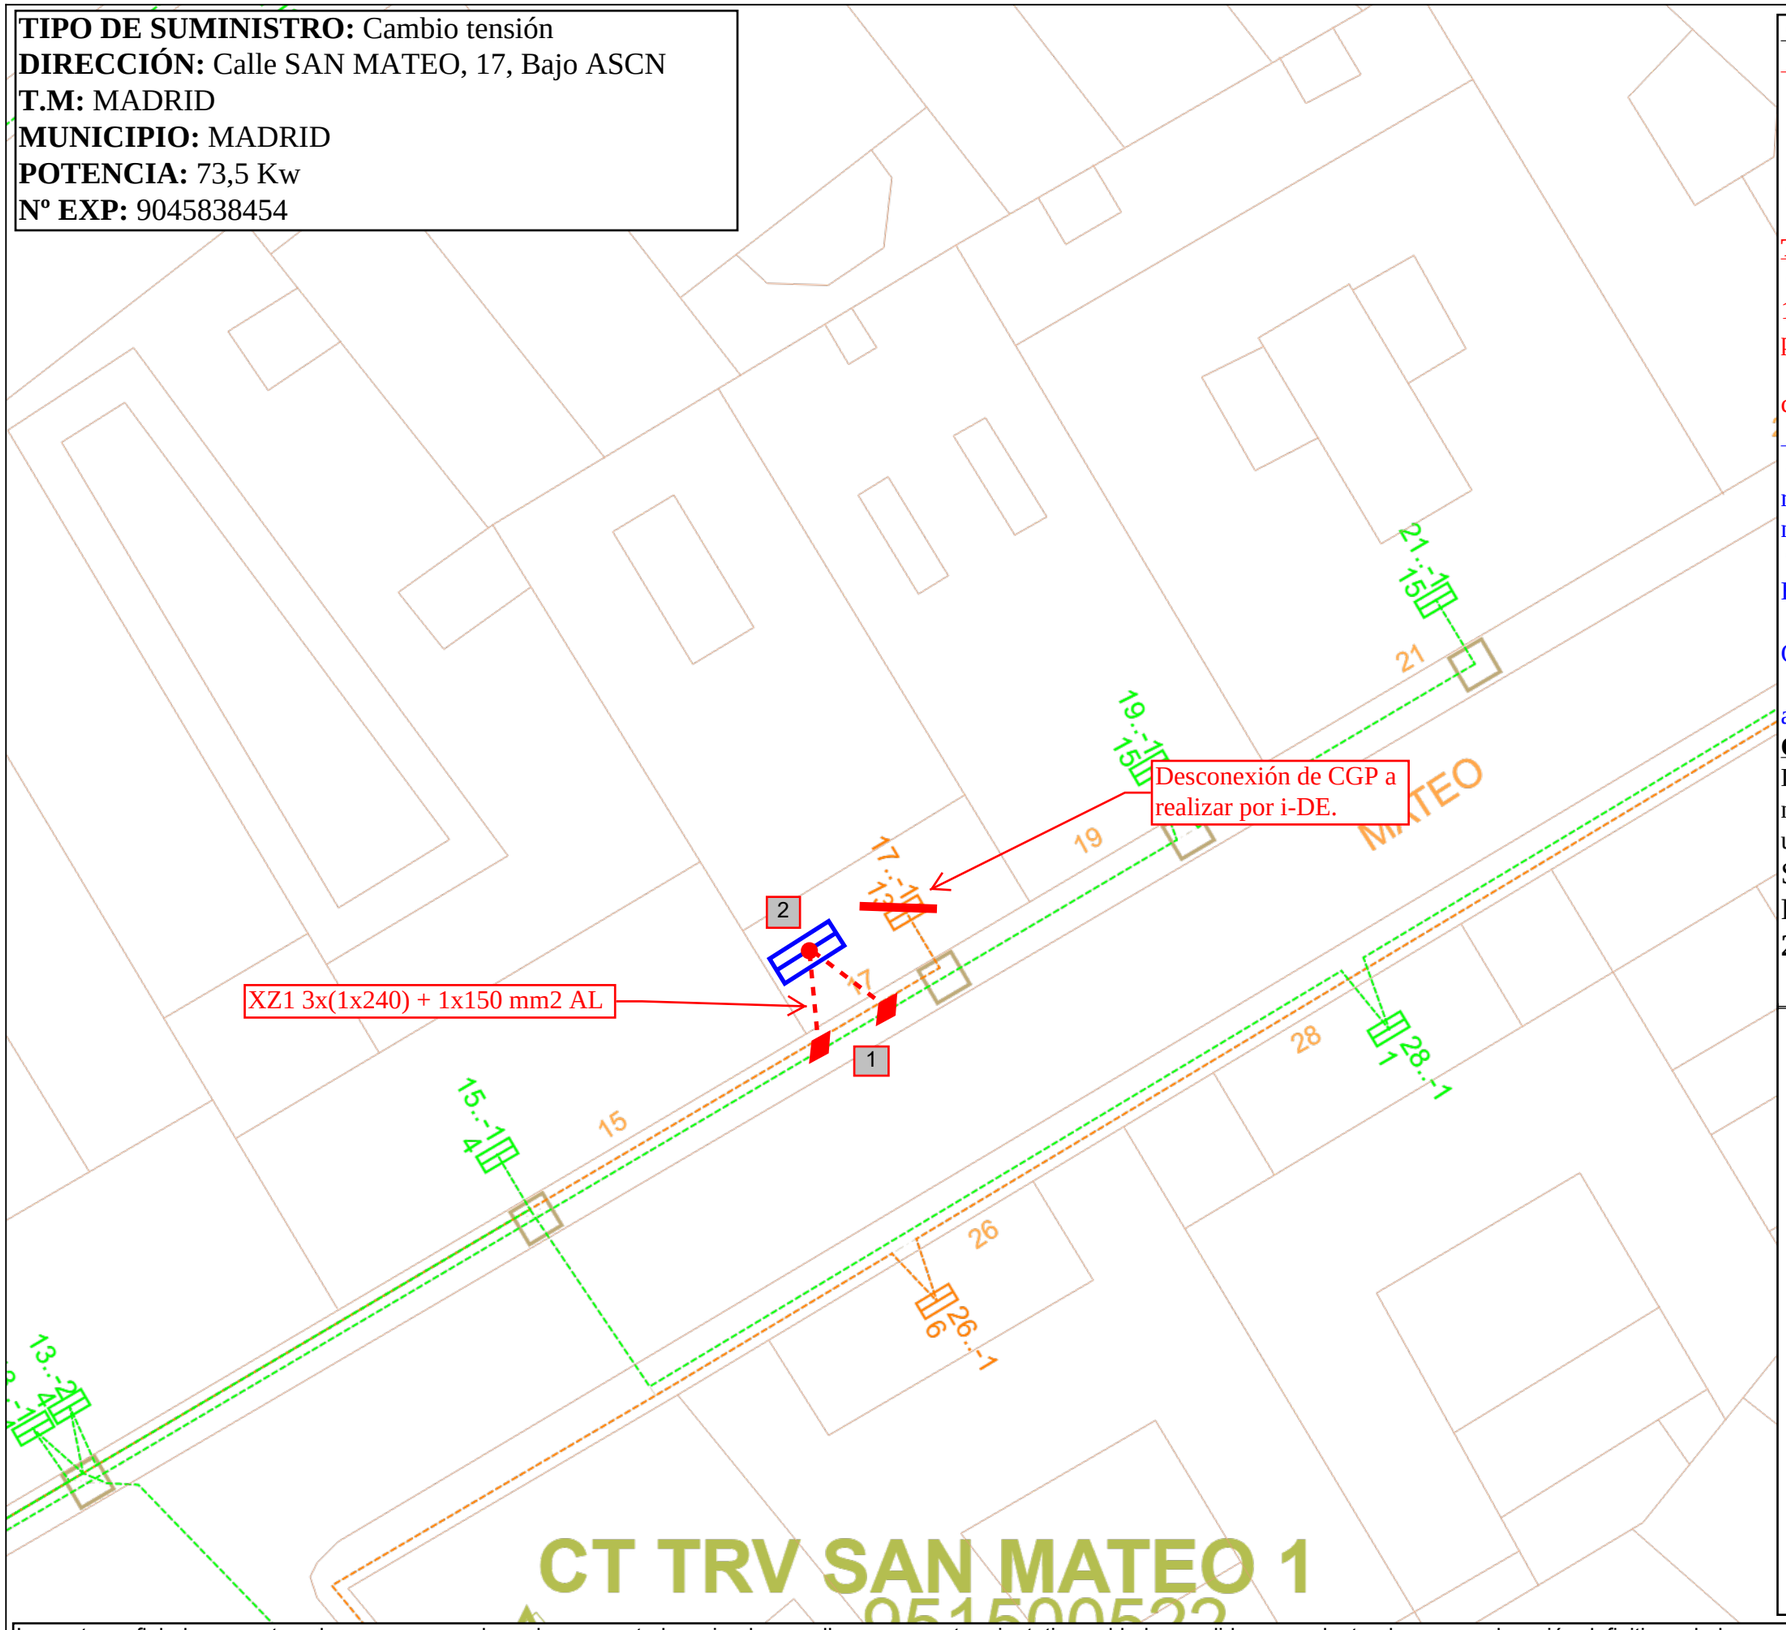

OBRA A REALIZAR

ENTRONQUE Y REFUERZO (a realizar por i-DE)

1.- Solicitud de permisos oficiales.
2.- Realizar (8) empalmes de tornillería en punto 1.
3.- Realizar (8) terminales de compresión en punto 2.
4.- Señalización de la nueva CGP ***(a instalar por el solicitante)***
5.- Desconexión de CGP existente.

TRABAJOS DE EXTENSIÓN (a realizar por i-DE)

6.- Apertura y posterior reposición de canalización con 4 tubos de 160 mm Ø Y 6 tubos de 160 mm Ø si discurre por calzada desde punto 1 a punto 2.
7.- Ejecutar tendido de cable XZ1 3x(1x150) + 1x95 mm2 AL por canalización realizada.


EXTENSION (A REALIZAR POR SOLICITANTE)

8. Instalar 2 mechinal a 40 cm sobre el nivel del suelo con 2 tubos rojos de 160 mm Ø + 1 tubo de 63 mm Ø enterrados a 80 cm bajo el nivel del suelo.
9.- Instalar 2 nuevas CGP -E10- homologada por I-DE, con bases BUC y fusibles.
10.- instalar puesta a tierra del neutro con cable tipo DN-RA 1X50 CU 50 mm2 normalizado por tubo rojo independiente de 63 mm Ø.
11.- Adecuar instalación de enlace para los suministros solicitados adaptandose a las especificaciones i-DE y conforme al REBT.

Observaciones


Debido a que su edificio tiene una tensión de 127/230 V no normalizada, se debe realizar el cambio de toda la finca pasando a una tensión de 230/400 V normalizada.
Se debe realizar la instalación de la CGP conforme al REBT y siguiendo las especificaciones i-DE del **MT 2.80.12 (19-05).**

Centro de tranformación
CT: SAN MATEO 7
Nº: 10100031
LÍNEA: 15

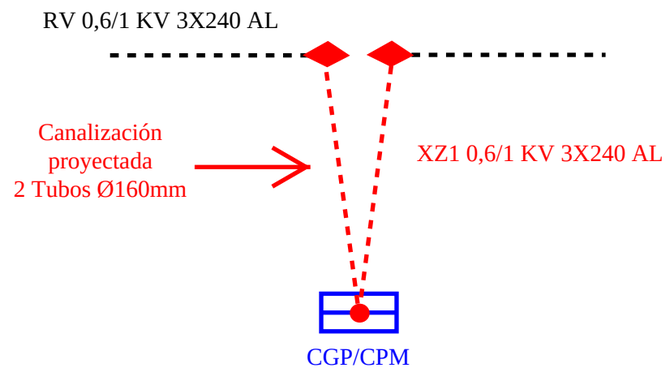


Las cotas reflejadas en estos planos corresponden a las proyectadas, siendo por ellos meramente orientativas al haber podido ser replanteadas en su ejecución definitiva o haberse modificado posteriormente las alineaciones y rasantes de referencia. Por lo que, dado su caracter orientativo, en todo caso, exigen de precia cata o calicata manual al inicio de la excavación realizada por personal cualificado, o barridos con georradar de la zona de trabajo para evitar cualquier incidencia con otras instalaciones, eléctricas o de cualquier otro tipo, existentes.


CANALIZACIÓN ENTUBADA EN ACERA CON ASIENTO DE ARENA (4 TUBO)

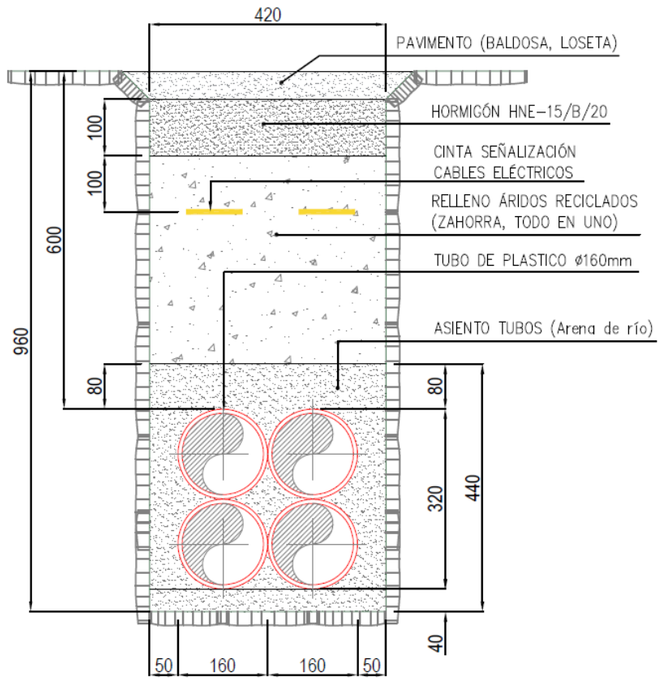

CANALIZACIÓN ENTUBADA EN CALZADA CON ASIENTO DE HORMIGÓN (6 TUBOS)

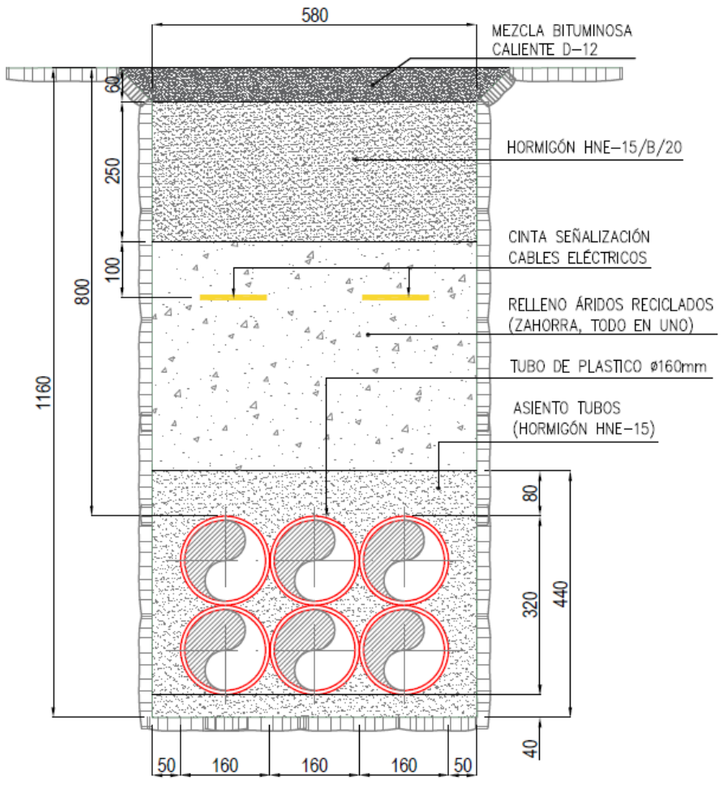

VISTA FRONTAL

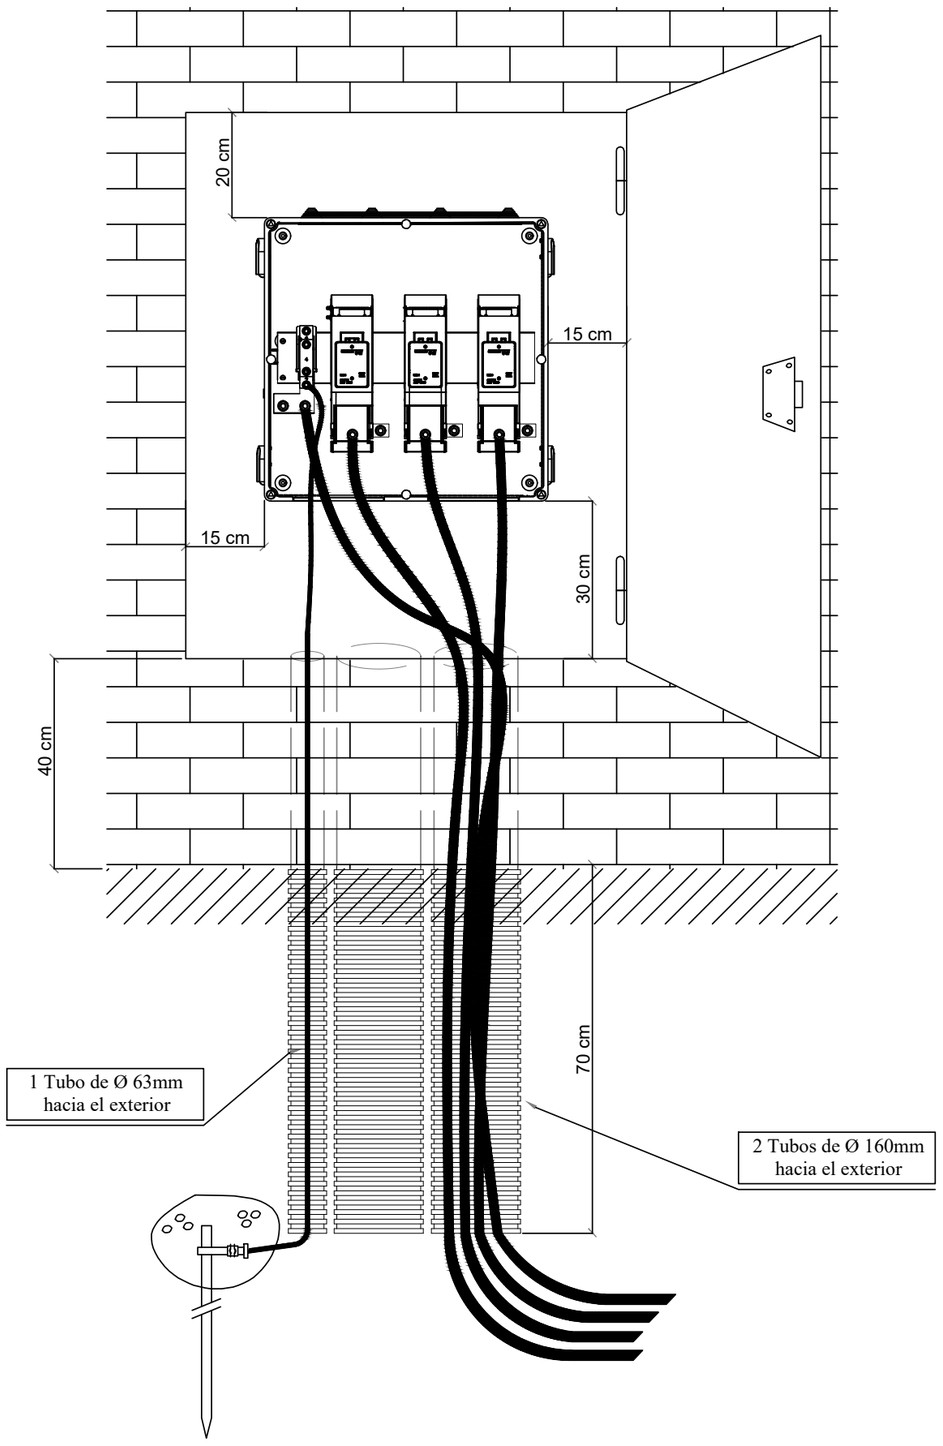

VISTA LATERAL

