
PROYECTO PARA LA AUTORIZACIÓN CONJUNTA ANUAL DE INSTALACIONES DE GAS CANALIZADO DURANTE EL AÑO 2025 EN LA COMUNIDAD DE MADRID

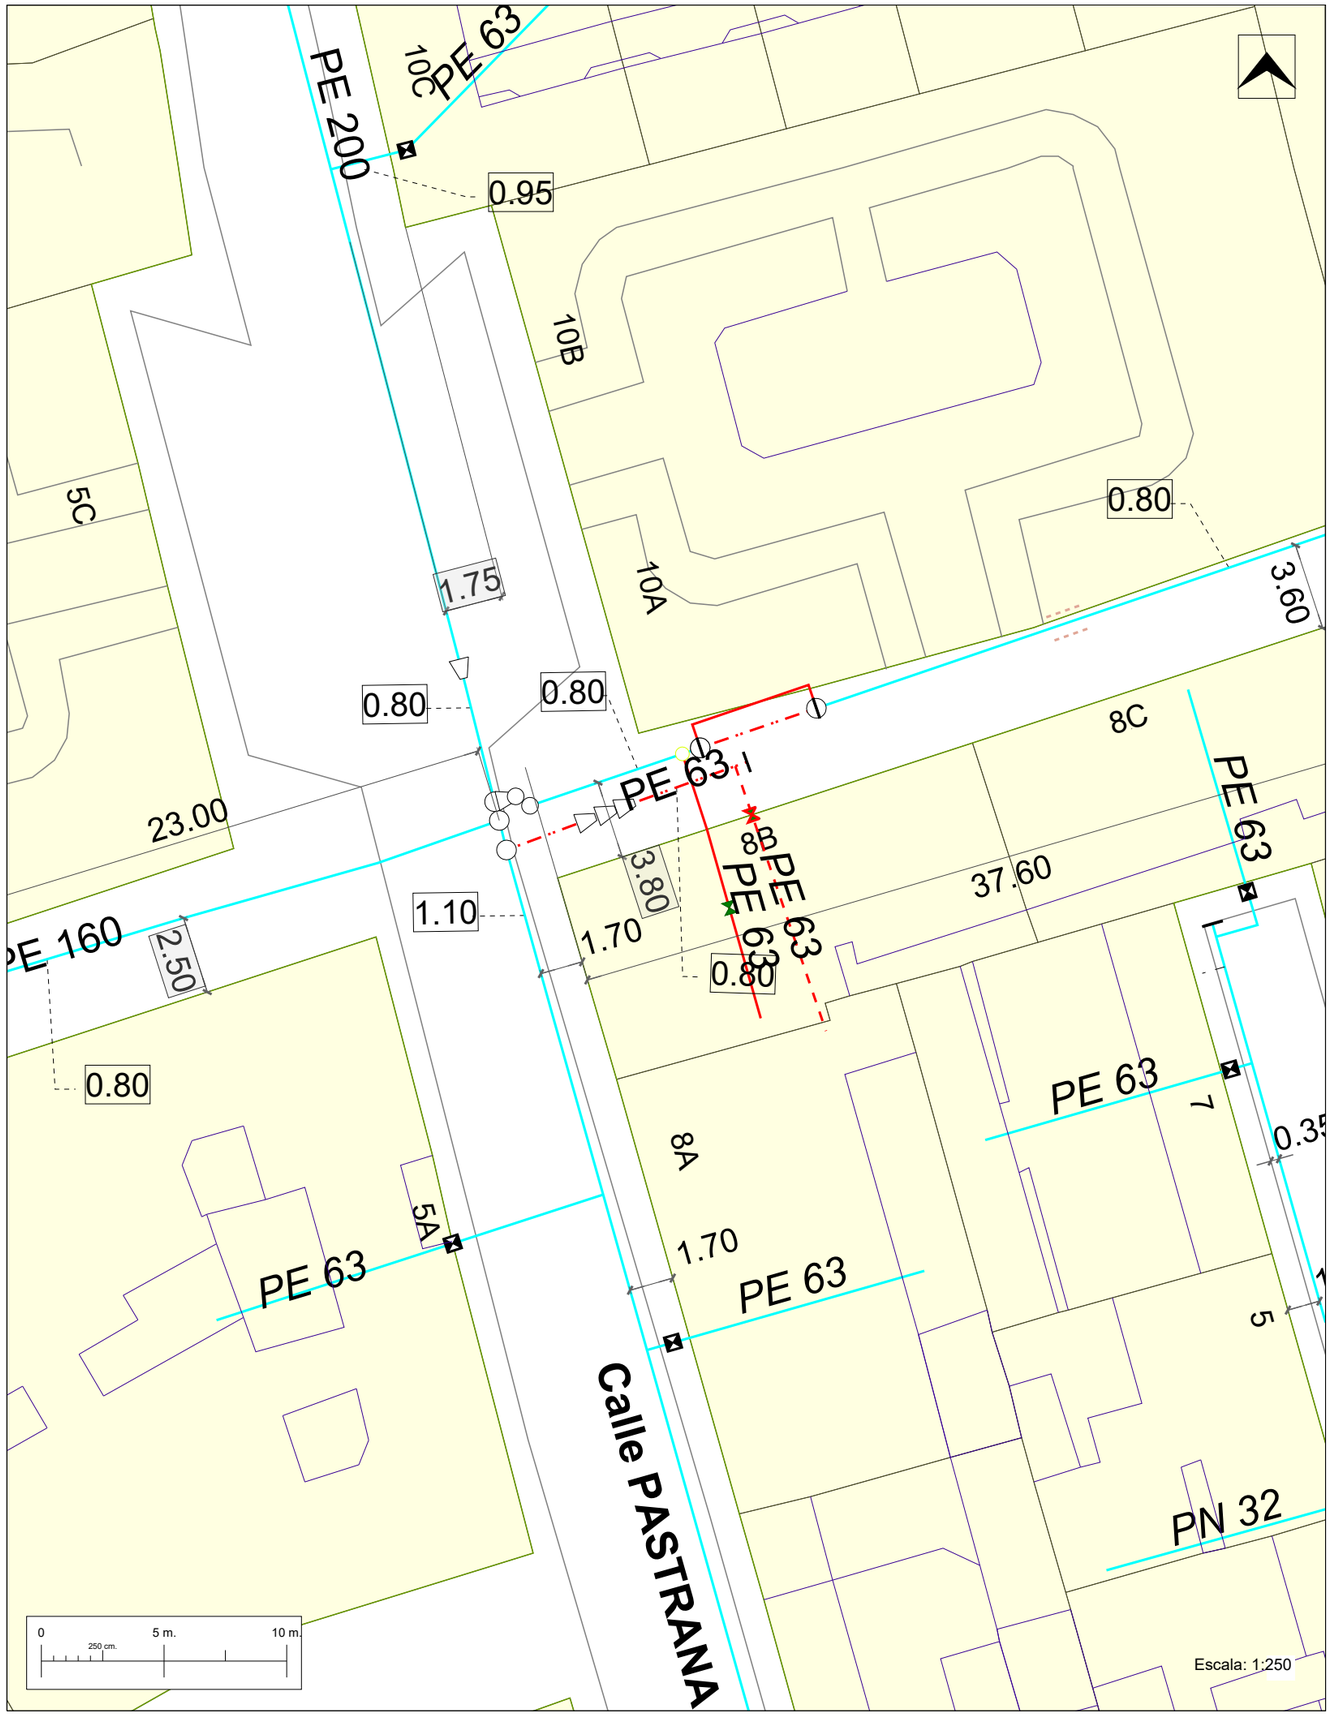

NEDGIA MADRID

Fecha	09/12/25
Dirección	PASTRANA 8B (DESPLAZAMIENTO RED)
Municipio	Madrid
Distrito	San Blas
Código Obra	022025649558
Tipo Obra	Desplazamiento de 3º
Formato	A3 H

AUTOR DEL PROYECTO


Alejandra Risco Barba

Ingeniero Técnico Industrial

MOP: 0.025 bar
OP: 0.025 bar

TIPO DE GAS: **GAS NATURAL**

Observaciones

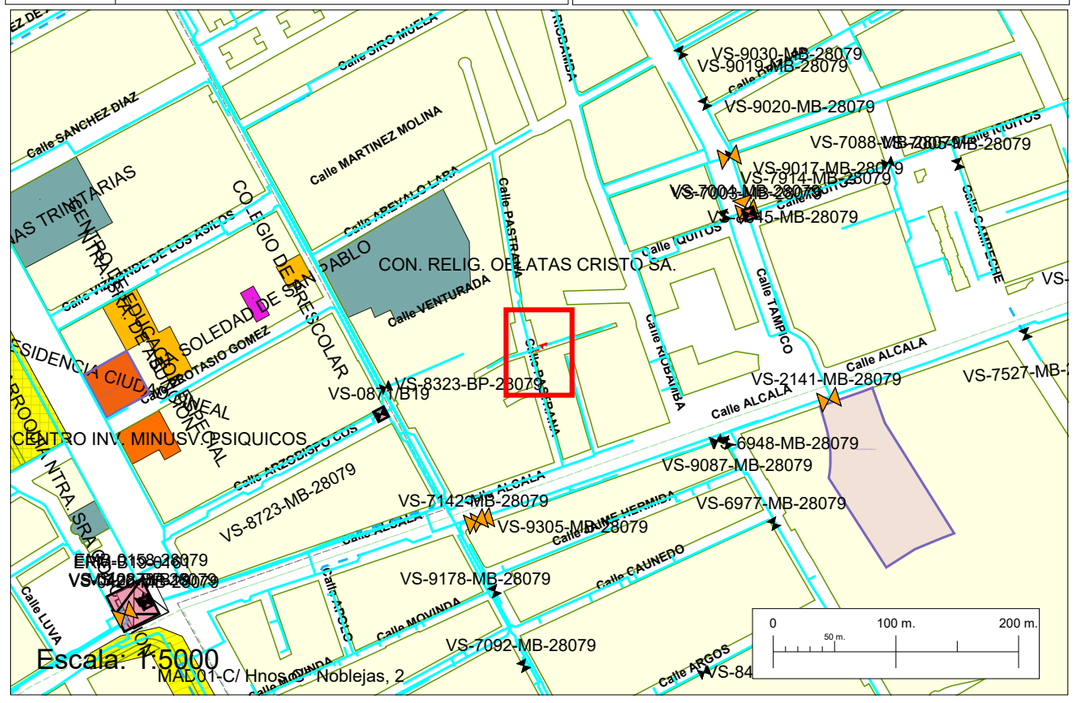

CARACTERÍSTICAS DE LA INSTALACIÓN

Canalización de profundidad => 0.60			Acometidas de profundidad =>0,30			
Longitud	Material	Diámetro	Unidades	Longitud	Material	Diámetro
10.00	Polietileno	110mm	1	3.80	Polietileno	63mm

Datos establecidos para la canalización

	Pavimentos (m2)	Apertura zanja (m)	Canalización	Acometidas	TOTAL
Aglomerado asfáltico		Acera Pavimentada	10.00	3.80	13.80
Losas de Piedra		Acera no Pavimentada			0.00
Adoquines		Calzada Pavimentada			0.00
Hormigón		Calzada no Pavimentada			0.00
Tierra		TOTAL			13.80
Losetas normales					
Losetas especiales	4.42				
TOTAL	4.42				

LEYENDA

- Acometida.Traza - Obra ejecutada
- Acometida.Traza - Por canalizar
- Acometida.Traza - A sustituir
- Subtramos de red.Traza - Obra ejecutada
- Subtramos de red.Traza - Por canalizar
- Subtramos de red.Traza - A dar de Baja